


Rev.	Date	Drawn	Description	Designed	Checked	Approved
2	22/04/2022	MMW/QKL	AMENDMENT TO ERSS LAYOUT	MMN/WHZ	MMN/WHZ	LHT
1	18/02/2022	MMW/QKL	PROPOSED ERSS @ I06 (due to adjustment of the pilecap location)	MMN/WHZ	MMN/WHZ	LHT
0	06/01/2022	MMW/QKL	PROPOSED ERSS @ I06	MMN/WHZ	MMN/WHZ	LHT

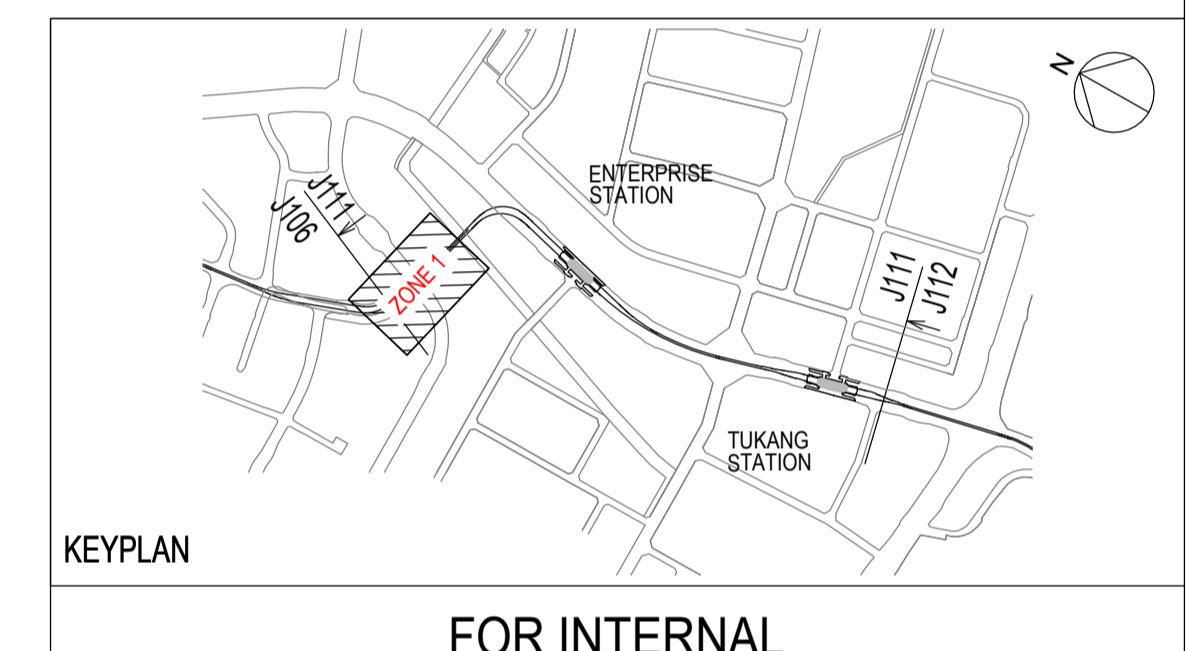

Land Transport Authority
Contractor : **HEC**
中国港湾 CHINA HARBOUR
Architect: **DPA DP ARCHITECTS** C&S and Building Services Consultant: **AECOM**

Project Title: CONTRACT J111
DESIGN AND CONSTRUCTION OF ENTERPRISE STATION, TUKANG STATION AND VIADUCT FOR JURONG REGION LINE

Drawing Title: PROPOSED ERSS LAYOUT - I06


Checked By: MAUNG MAUNG NYUNT Checked By: WU HAIZHANG Approved By: LIE HAI THAW

Scale N.T.S Drawn By: MYO MOYO WIN/ QIN KUAILE Date 18/02/2022


Drawing No: D/J111/ERSS/I06/0002 Status Rev. 2

Model Name: Sheet: 1 of 3 A1

Pier No.	Location	Affected utilities	Treatment		Appendix Z Recorded?	Clearance from External Surface of ERSS after Treatment (m)			Action / follow up note	LTA-Trial Trench		CHEC-Trial Trench					
			Proposed Treatment	Action By		Code Required	Nearest actual dimension	Comply?		Trial Trench No.	Date	Trial Trench Done		Trial Trench Proposed			
												Trial Trench	Date	Trial Trench	Target Date		
I06	Jurong West St64	SingTel	To Protect	CHEC	N	1	1.49	YES	*To produce MS (bore piling, sheet piles driving) with protection of 8W and submit to SingTel to get approval. * Adjust ERSS location	TT#28B	25/08/2017	TH#31A	14.10.2021	2	21/01/2022		
I06	Jurong West St64	Sewer	To Retain	NA	N	2	1.9	NO	*To produce MS (bore piling, sheet piles driving) and submit to PUB to get approval. * Adjust ERSS location	0	NA	0	NA	0	NA		

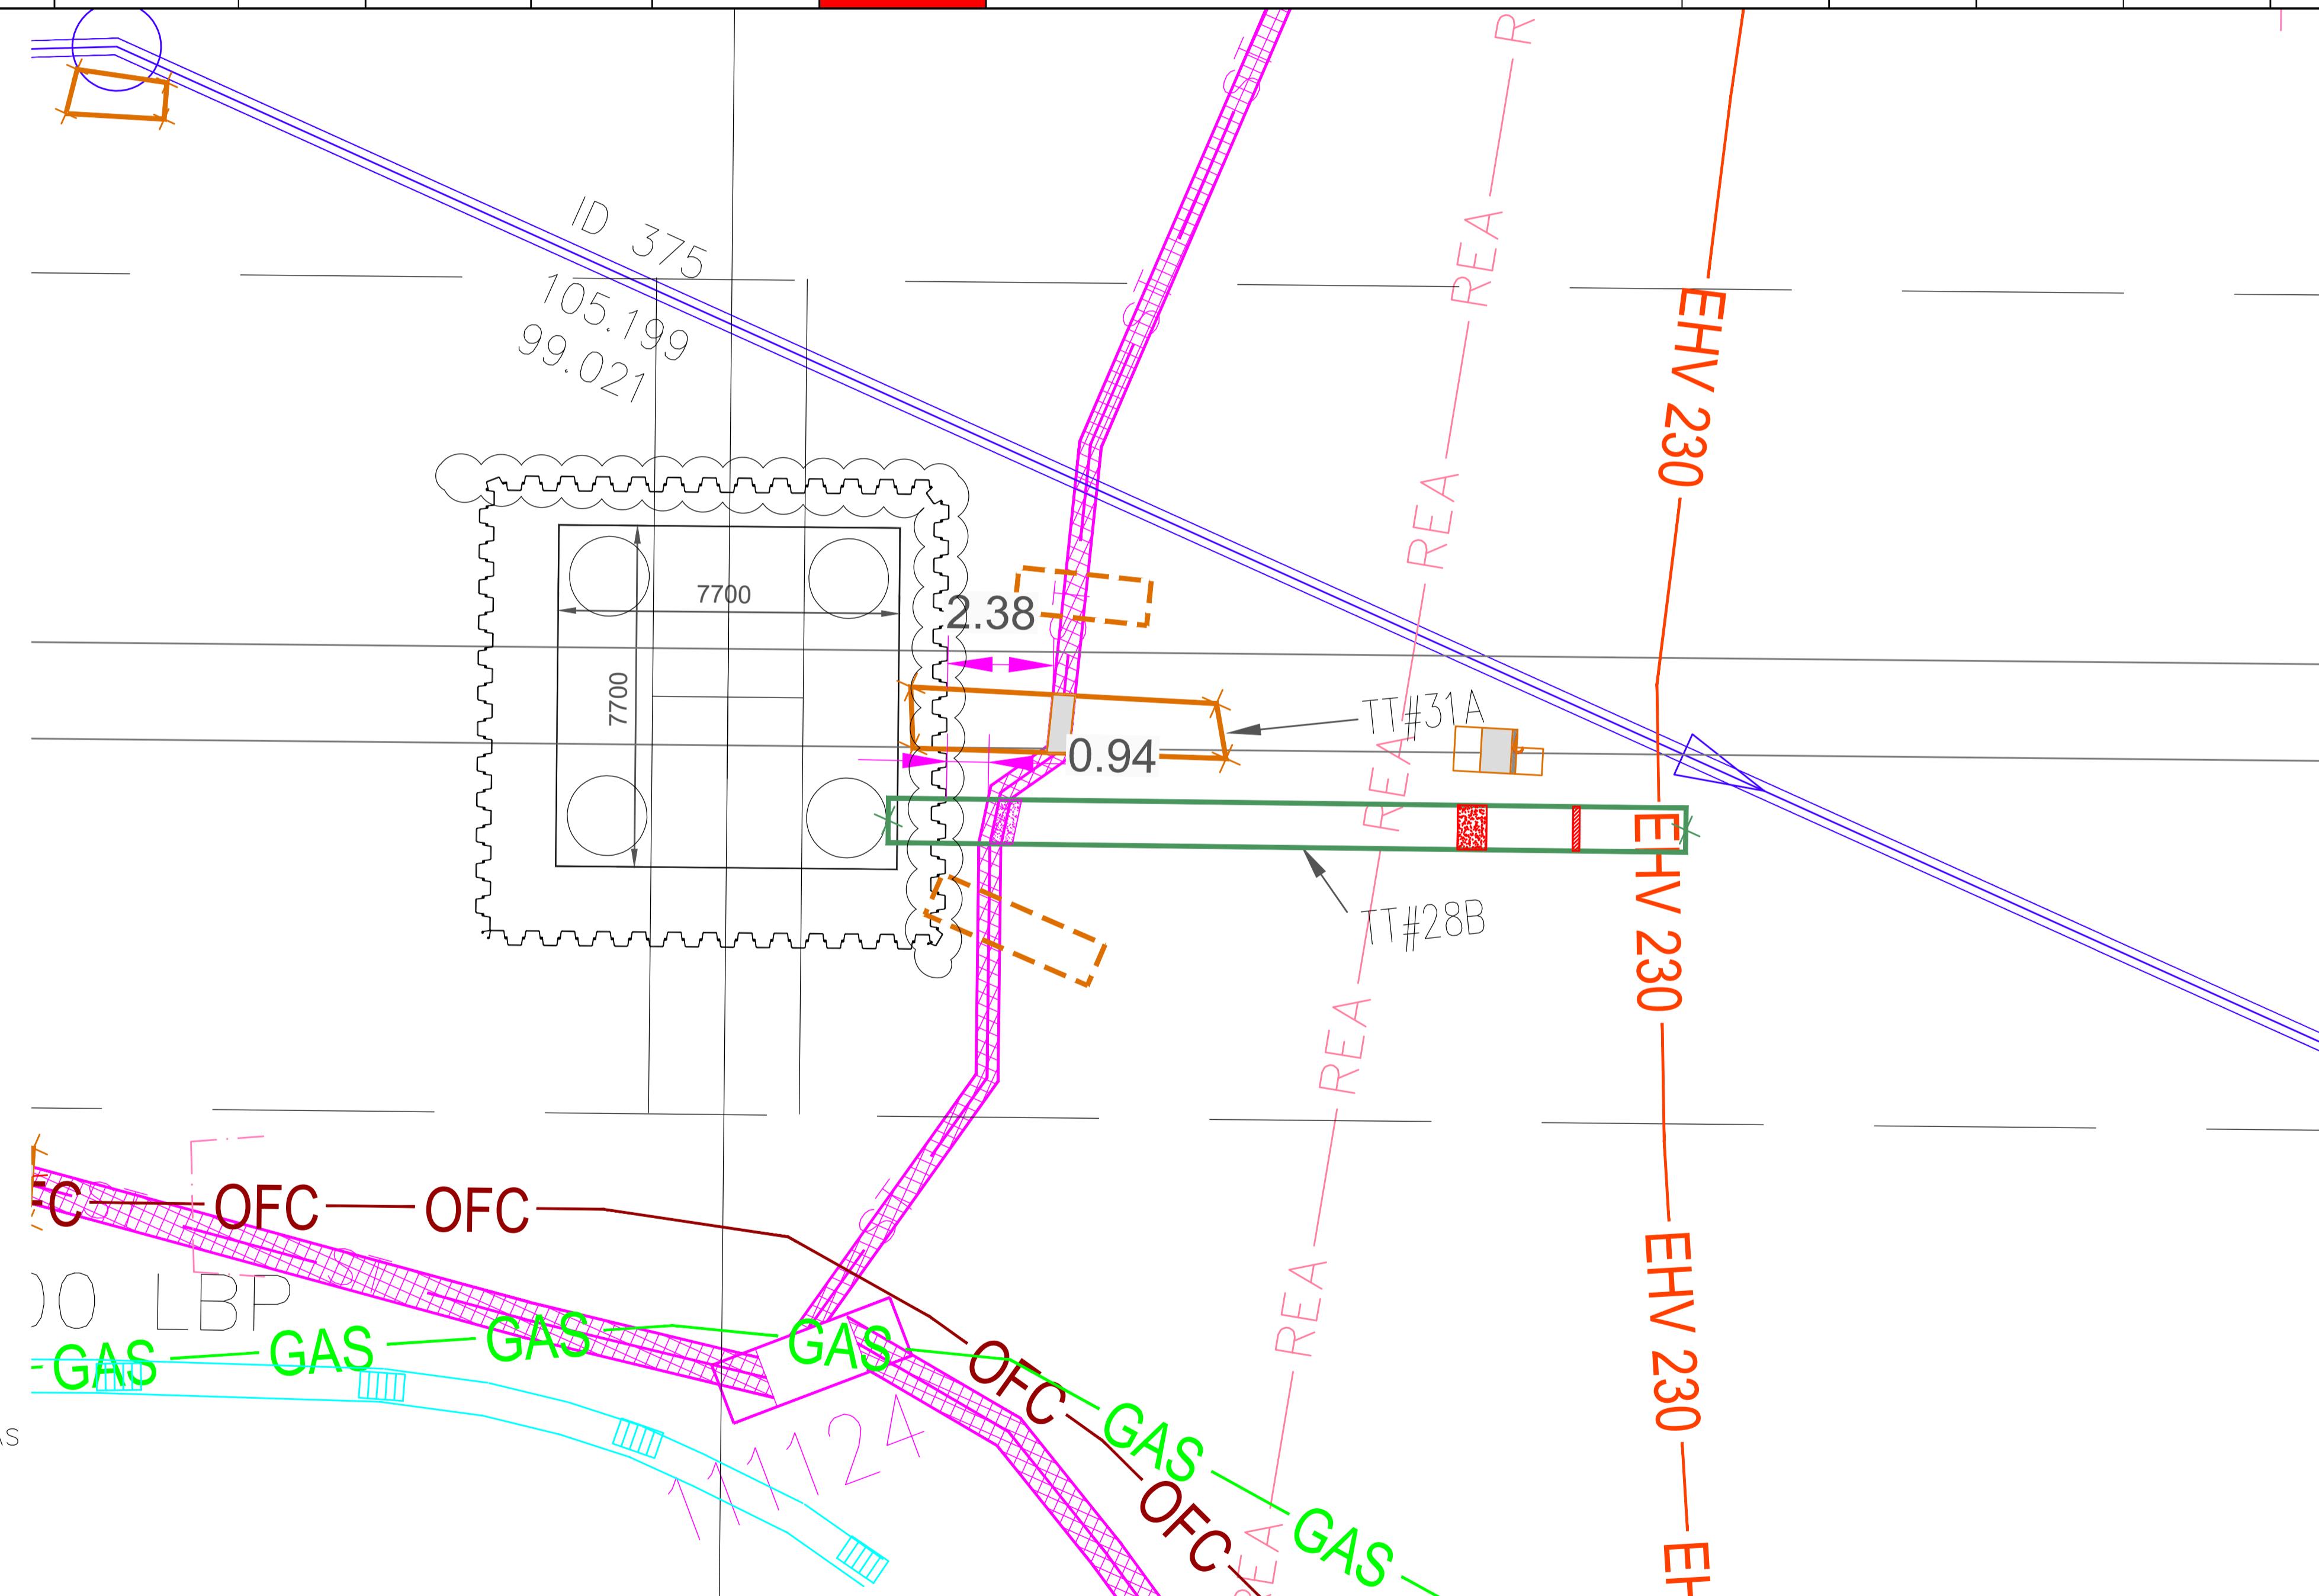

Rev.	Date	Drawn	Description	Designed	Checked	Approved
2	22/04/2022	MMW/QKL	AMENDMENT TO ERSS LAYOUT	MMN/WHZ	MMN/WHZ	LHT
1	18/02/2022	MMW/QKL	PROPOSED ERSS @ I06 (due to adjustment of the pilecap location)	MMN/WHZ	MMN/WHZ	LHT
0	06/01/2022	MMW/QKL	PROPOSED ERSS @ I06	MMN/WHZ	MMN/WHZ	LHT

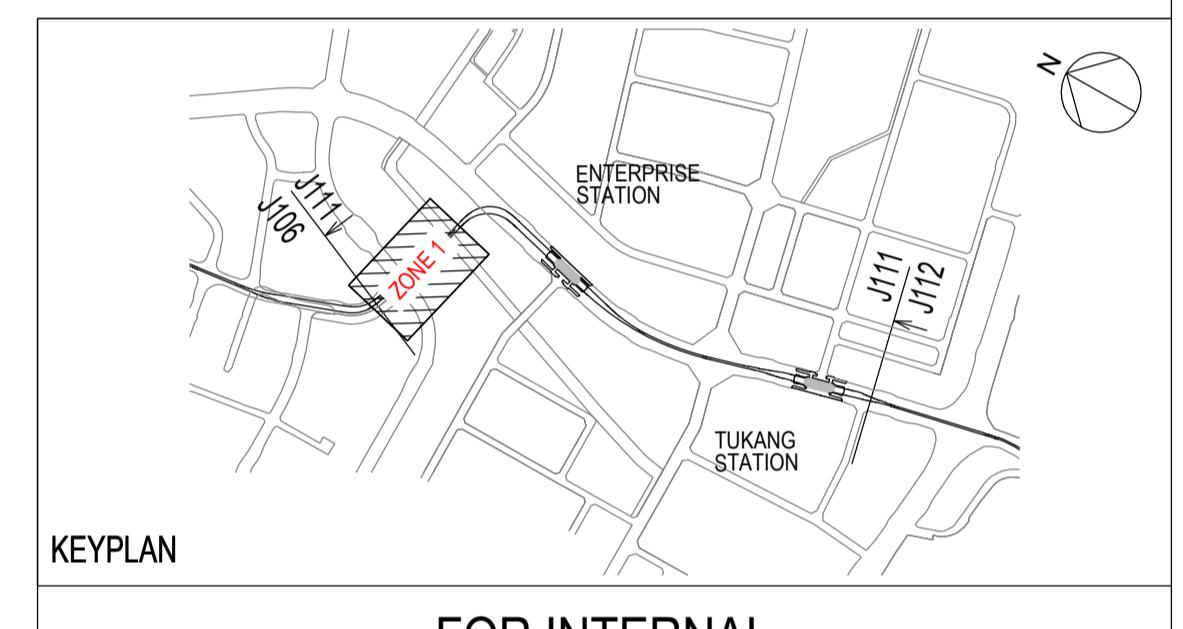

Land Transport Authority

Contractor : **CHEC**
Architect: **DPA DP ARCHITECTS** C&S and Building Services Consultant: **AECOM**

Project Title: CONTRACT J111
DESIGN AND CONSTRUCTION OF ENTERPRISE STATION, TUKANG STATION AND VIADUCT FOR JURONG REGION LINE



Drawing Title: PROPOSED ERSS LAYOUT - I06

Checked By: MAUNG MAUNG NYUNT Checked By: WU HAIZHANG Approved By: LIE HAI THAW


Scale N.T.S Drawn By: MYO MOYO WIN/ QIN KUAILE Date 22/04/2022

Drawing No: D/J111/ERSS/I06/0002 Status Rev. 1

Model Name: Sheet: 2 of 3 A1

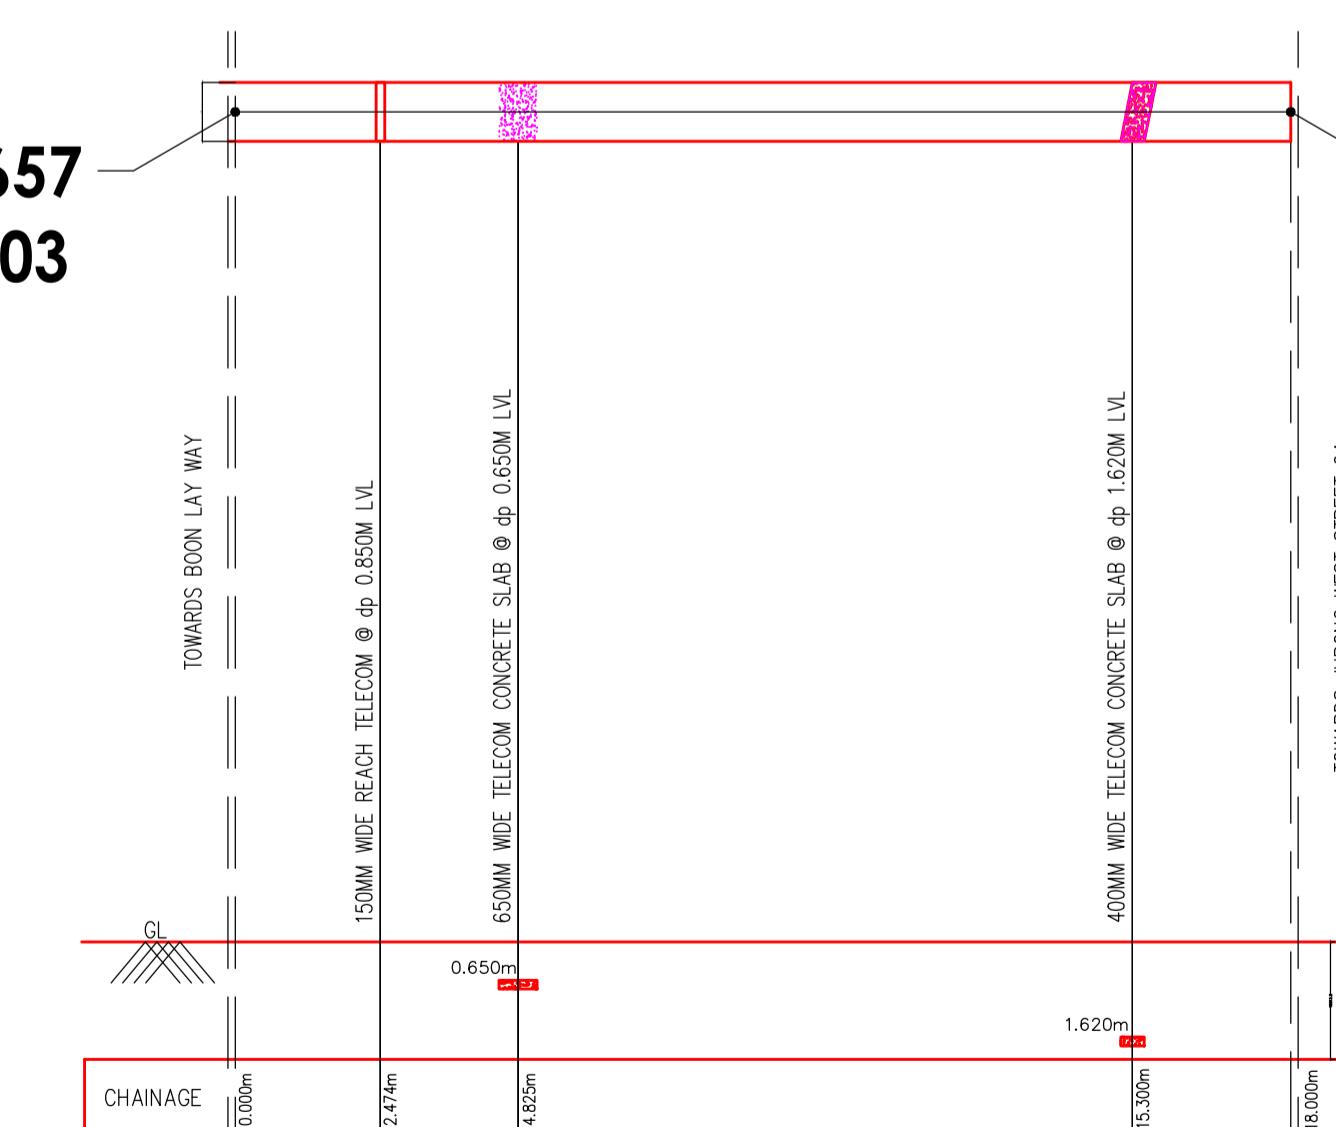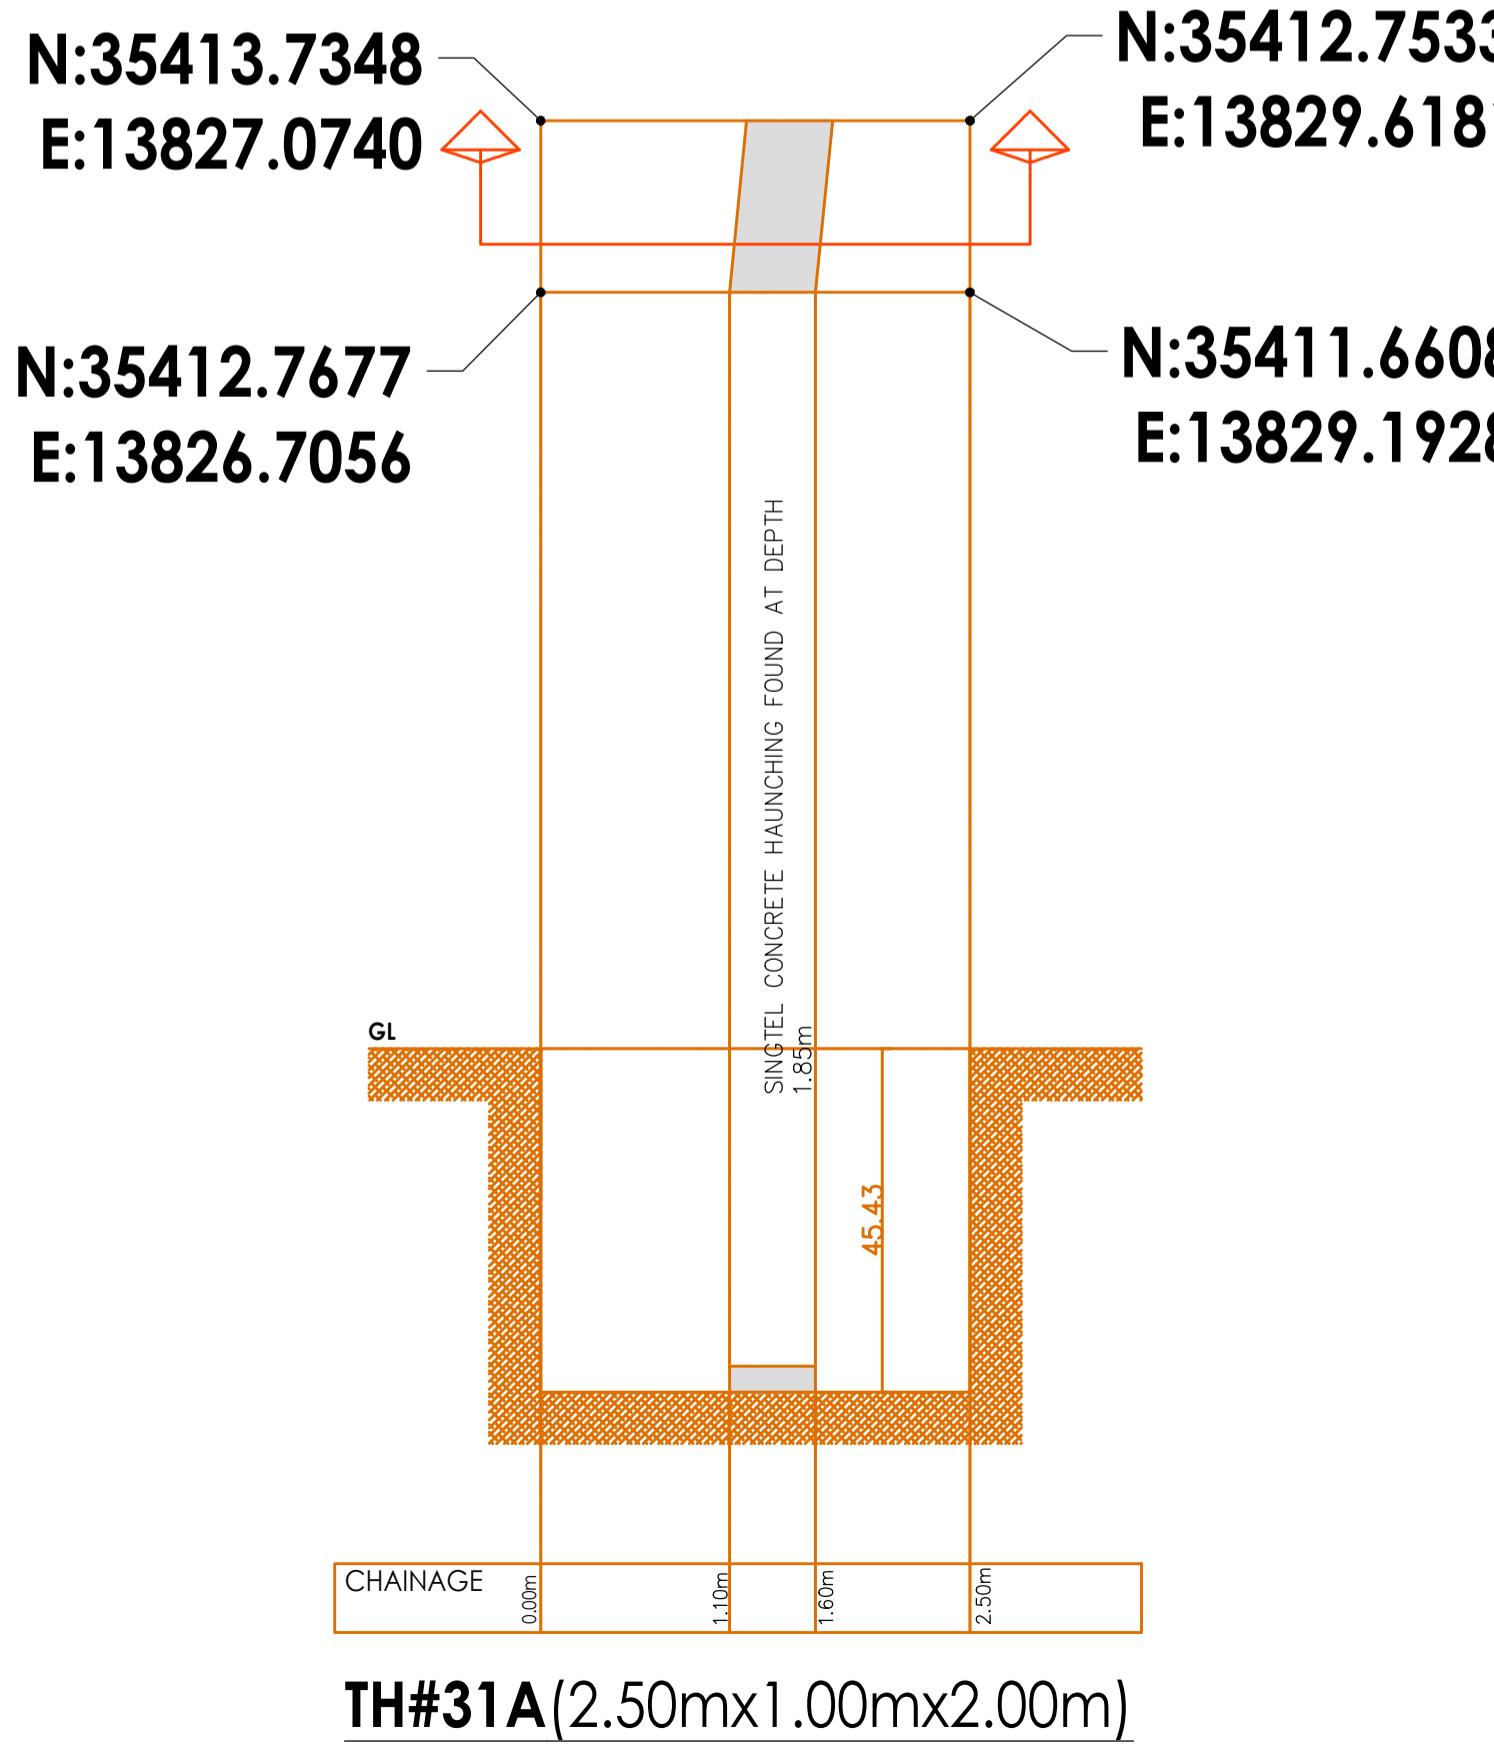

1	18/02/2022	MMW/QKL	PROPOSED ERSS @ I06 (due to adjustment of the pilecap location)	MMN/WHZ	MMN/WHZ	LHT
0	06/01/2022	MMW/QKL	PROPOSED ERSS @ I06	MMN/WHZ	MMN/WHZ	LHT
Rev.	Date	Drawn	Description	Designed	Checked	Approved

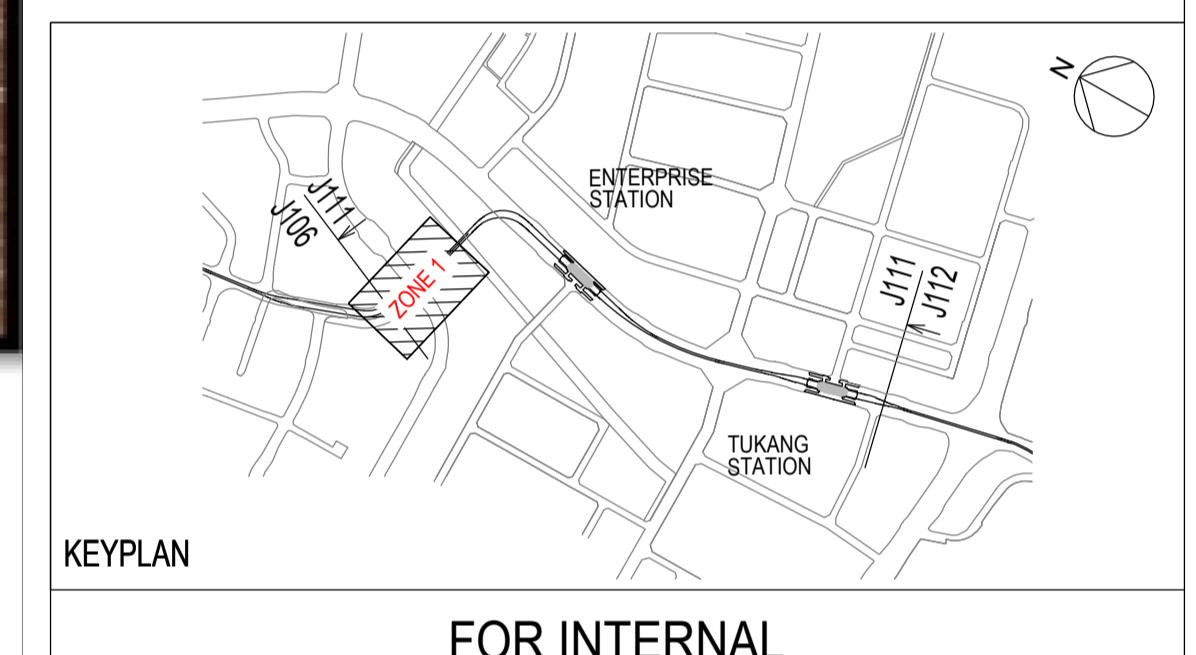

Land Transport Authority

Contractor :



中国港湾
CHINA HARBOUR

Architect :



C&S and Building Services Consultant:
AECOM

Project Title:

CONTRACT J111
DESIGN AND CONSTRUCTION OF ENTERPRISE STATION, TUKANG STATION AND VIADUCT FOR JURONG REGION LINE

Drawing Title:

PROPOSED ERSS LAYOUT - I06

Checked By: MAUNG MAUNG NYUNT	Checked By: WU HAIZHANG	Approved By: LIE HAI THAW
----------------------------------	----------------------------	------------------------------

Scale N.T.S	Drawn By: MYO MOYO WIN/ QIN KUAILE	Date 18/02/2022
----------------	--	--------------------

Drawing No: D/J111/ERSS/I06/0002	Status	Rev. 0
-------------------------------------	--------	-----------

Model Name:	Sheet: 3 of 3	A1
-------------	---------------	----